

План фундамента Фм1 М 1:25

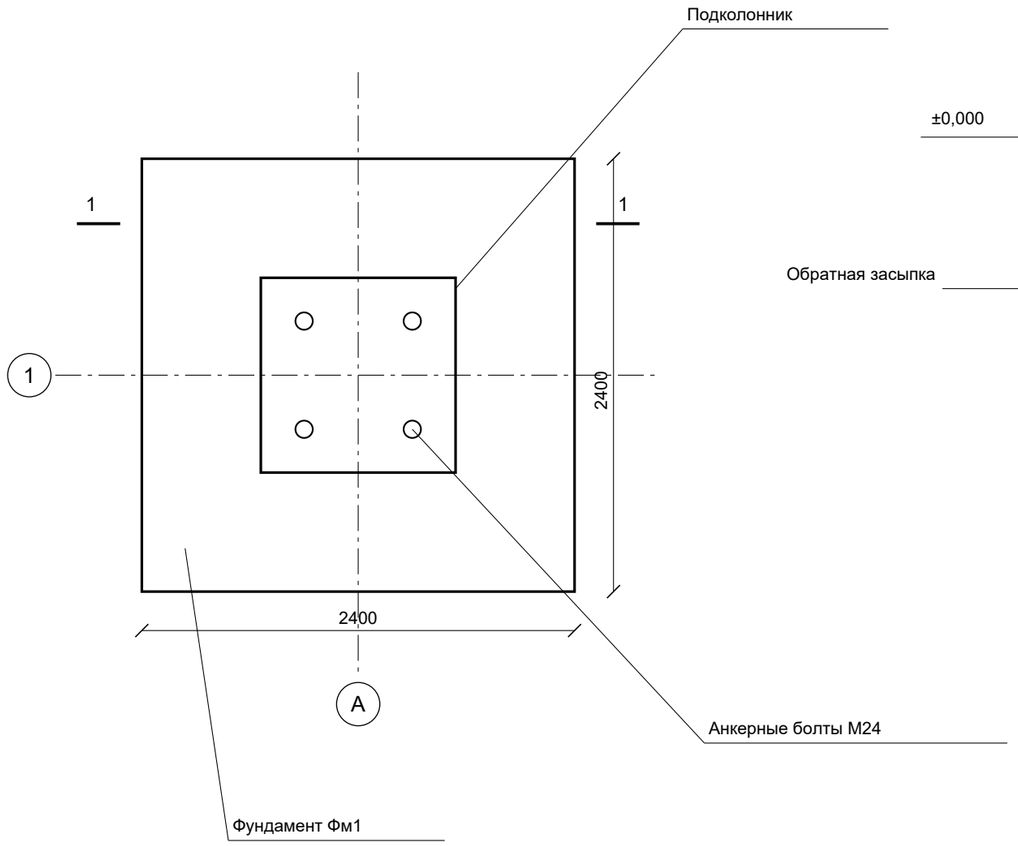

Разрез 1-1

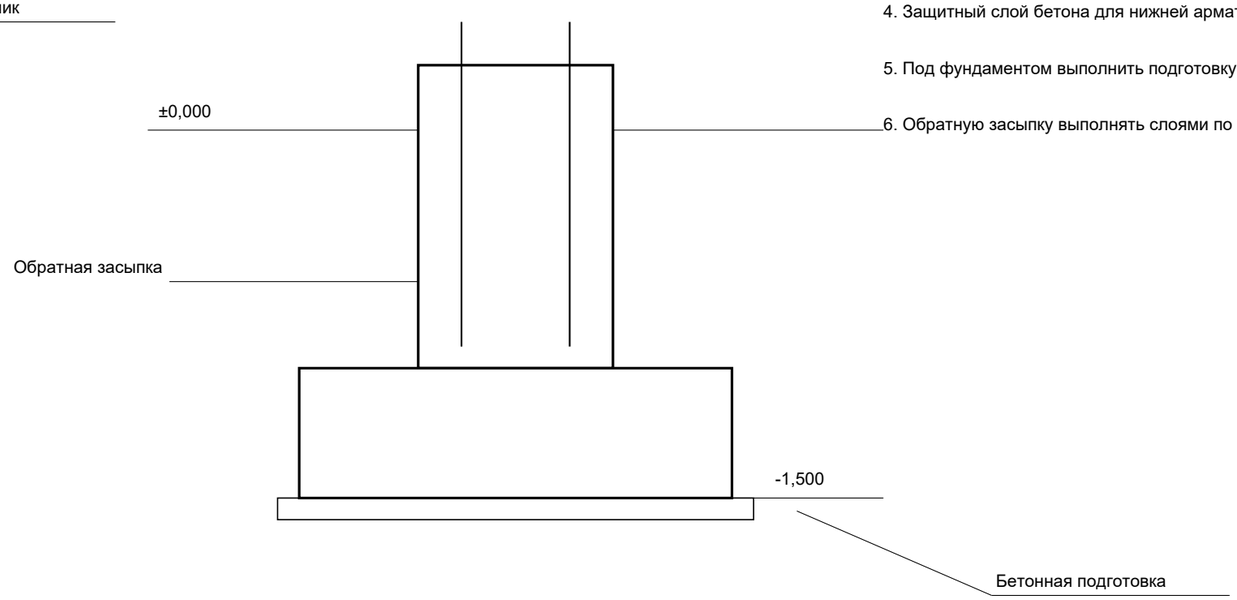

Примечания

1. Размеры даны в миллиметрах, отметки - в метрах.
2. Бетон фундамента класса В25 W6 F150 по ГОСТ 26633-2015.
3. Арматура класса А500С по ГОСТ 34028-2016.
4. Защитный слой бетона для нижней арматуры 40 мм.
5. Под фундаментом выполнить подготовку из бетона В7,5 толщиной 100 мм.
6. Обратную засыпку выполнять слоями по 300 мм с уплотнением.

Спецификация

Поз.	Обозначение	Наименование	Кол.	Масса ед., кг	Примечание
1	ГОСТ 34028-2016	Ø12 А500С, L=2350	24	2,09	
2	ГОСТ 24379.1-2012	Болт фундаментный М24	4	5,6	с гайками
3		Бетон класса В25			4,2 м³
4		Бетон класса В7,5			0,6 м³

Изм.	Кол.уч.	Лист	№док.	Подп.	Дата
Разраб.		Иванов			
Пров.		Петров			
Н.контр.		Сидоров			
ГИП		Кузнецов			

Насосная станция. Фундаменты под оборудование

План фундамента Фм1.
Разрез 1-1. Спецификация

Стадия	Лист	Листов
Р	1	2

ООО «Проектное бюро»

Взам. инв. №

Подп. и дата


Инв. № подл.

Общие данные
General data

Ведомость рабочих чертежей основного комплекта
List of working drawings of the main set

Лист Sheet	Наименование Title	Примечание Note
1	Общие данные General data	
2	План фундамента Фм1. Разрез 1-1. Спецификация Foundation Fm1 plan. Section 1-1. Specification	

Схема расположения фундаментов
Foundation layout

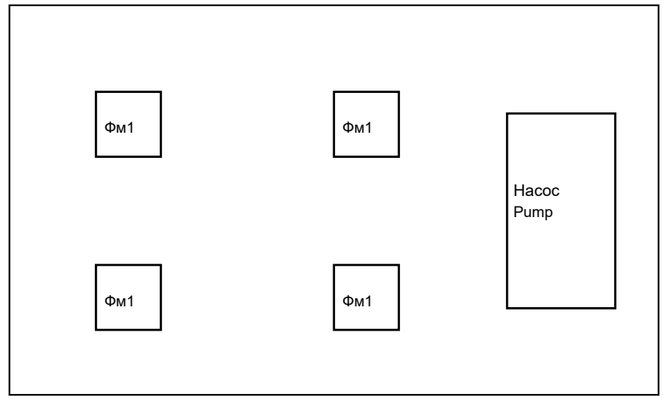

Общие указания
General notes

1. Проект разработан в соответствии с СП 22.13330.2016 и СП 63.13330.2018.
1. The design is developed in accordance with SP 22.13330.2016 and SP 63.13330.2018.

2. За отметку 0,000 принята отметка чистого пола насосной станции.
2. Elevation 0.000 is the finished floor level of the pumping station.

3. Основанием фундамента служит суглинок тугопластичный.
3. The foundation rests on stiff loam.

4. Перед бетонированием выполнить приемку арматуры с составлением акта.
4. Reinforcement shall be accepted with a report before concreting.

5. Работы выполнять в соответствии с проектом производства работ.
5. Works shall be carried out according to the work execution plan.

Взам. инв. №

Подп. и дата

Инв. № подл.

Изм.	Кол.уч.	Лист	№док.	Подп.	Дата
Разраб.		Иванов			
Пров.		Петров			
Н.контр.		Сидоров			
ГИП		Кузнецов			

Насосная станция. Фундаменты под оборудование

Общие данные

Стадия	Лист	Листов
Р	2	2

ООО «Проектное бюро»